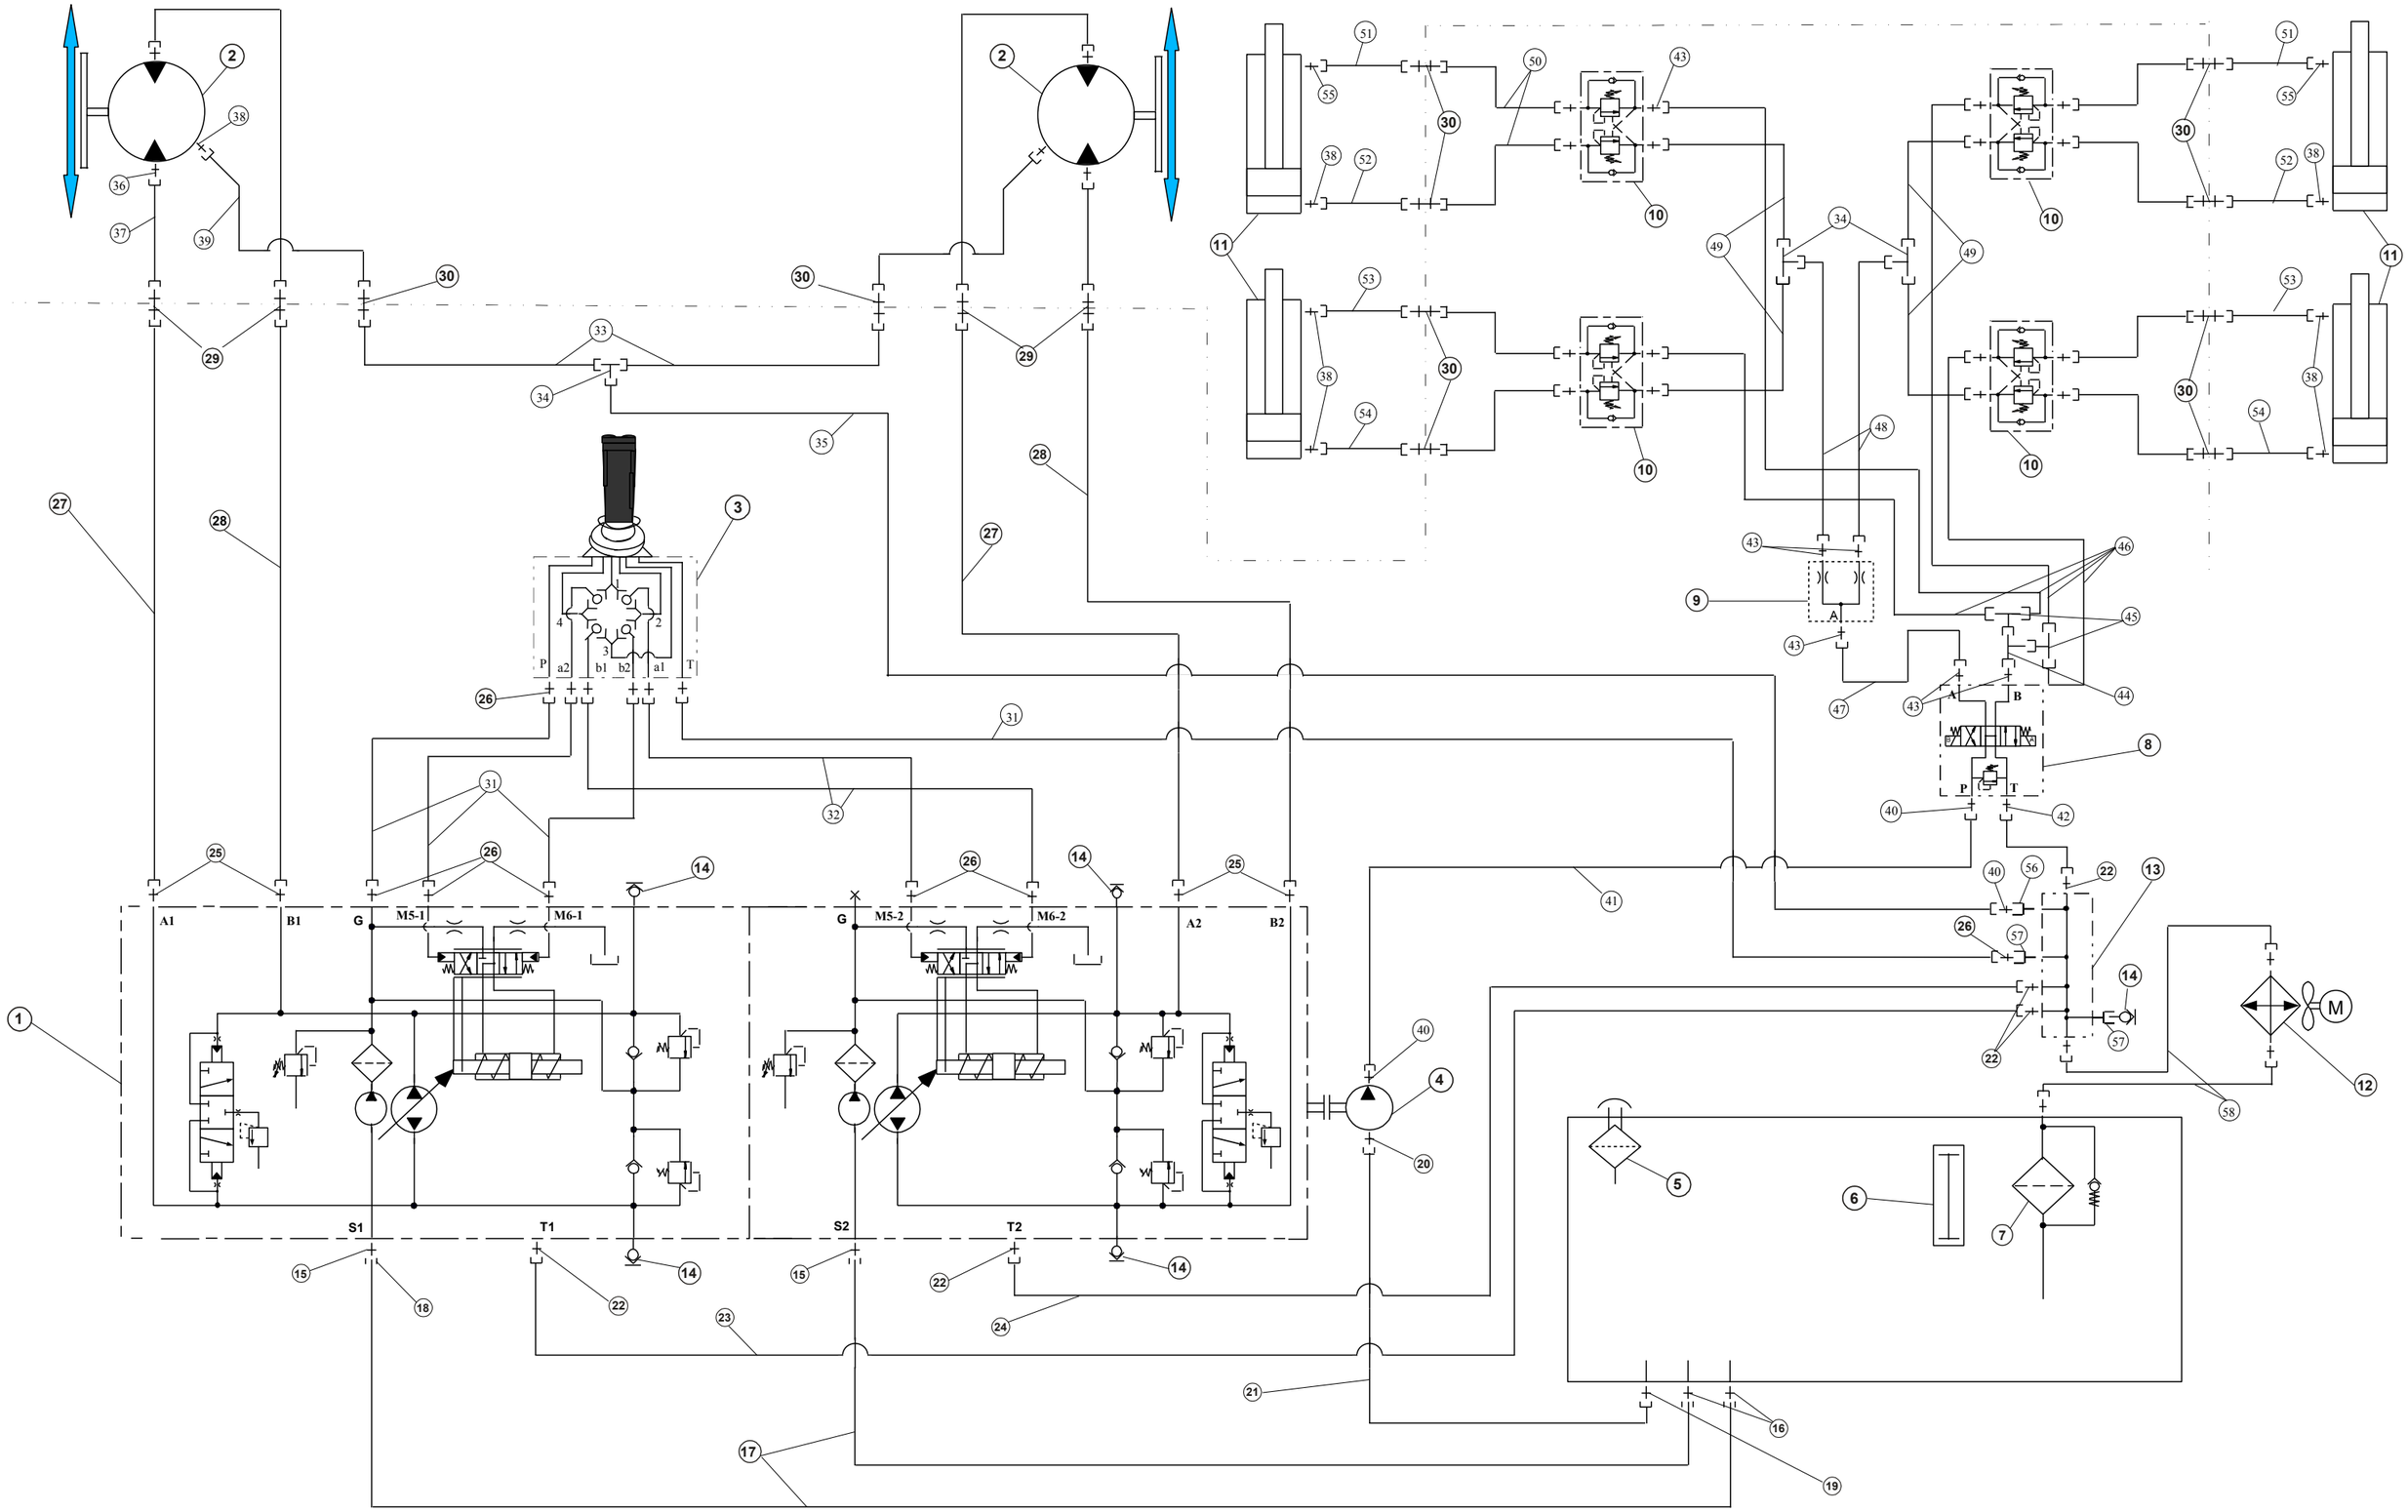


A1	../../..		...	...	...	Dessiné par : Martineau Matthieu
A0	21/09/10	Etablissement du plan		...	...	
IND	DATE	NATURE DE LA MODIFICATION	Dessiné par	Controlé par	Approuvé par	

DESIGNATION : IGUANA AMPHIBOAT

CLIENT :

Ce document est la propriété d'Hydrokit, copie, communication et utilisation interdites sauf autorisation écrite

HydrokiT
HYDRAULIC GLOBAL SOLUTIONS